



**שכונה**  
הצפון הישן - החלק הדרומי

**שימושים נוספים**  
פעילות פנאי, תרבות, אמננות והעשרה לכל הגילאים, לצד חוגים ופעילות  
 ثنائية קבועה

**סוג הנקודה**  
מרכזית  
מרכזת מספר\_Programot\_mashlevot\_kahilot\_shonot

**כלי תוספת**  
מבנים בעלי שימושים מסוימים בעיר מאפשרים לשימושים נוספים ול מגוון משתמשים להשתלב  
בינם. מבנים קהילתיים פרושים ברחבי העיר ומהווים מוקדים משמעותיים לכל התושבים בכל  
הגילאים, ובאופן טבעי יכולים גם קהילות נוספות. התוספת קבועה וממוקמת במהלך רציף עם הרחוב,  
בקומת הקרקע של המבנה הקהילתי ומאפשרת למשתמש בחירה.  
התוספות מורכבות אלמנטים עיצוביים המאפיינים שפה רכה כגון, שוקת וקירות מרוחף המאפשר  
ונטולzie טבעיות, המאפשרת מפגש אנושי מרובה.


## אודות


המרכז הקהילתי אינשטיין ממוקם בין הרחובות פרוג ודב הוז שבצפון העיר. למבנה מראשית ימי  
משמעות חינוכית, שימש כבית צערות מזרחי, פנימיה ובית ספר מקצועי לבנות.

כיום משמש כמרכז קהילתי פעיל בעל שימושים ומשתמשים רבים מדי יום, ומטרתו להיות הבית  
 הציבורי של תושבי האזור.


בעיר חסרים מענים וסיעת רפואי מיידי, משתמשים בעלי קשיי התניידות וקשיי למול החוק נותרים  
לא מצוי פעים רבים בהקשר זה. פרישת המרכזים הקהילתיים הקיימת בעיר, מאפשרת חיבור  
טבעי לתוך הסיעת רפואי, מתוך היותם נקודת ניקוז קהילתית אינטואיטיבית.

## 濟ع רפואי | מבט אדרוי

 


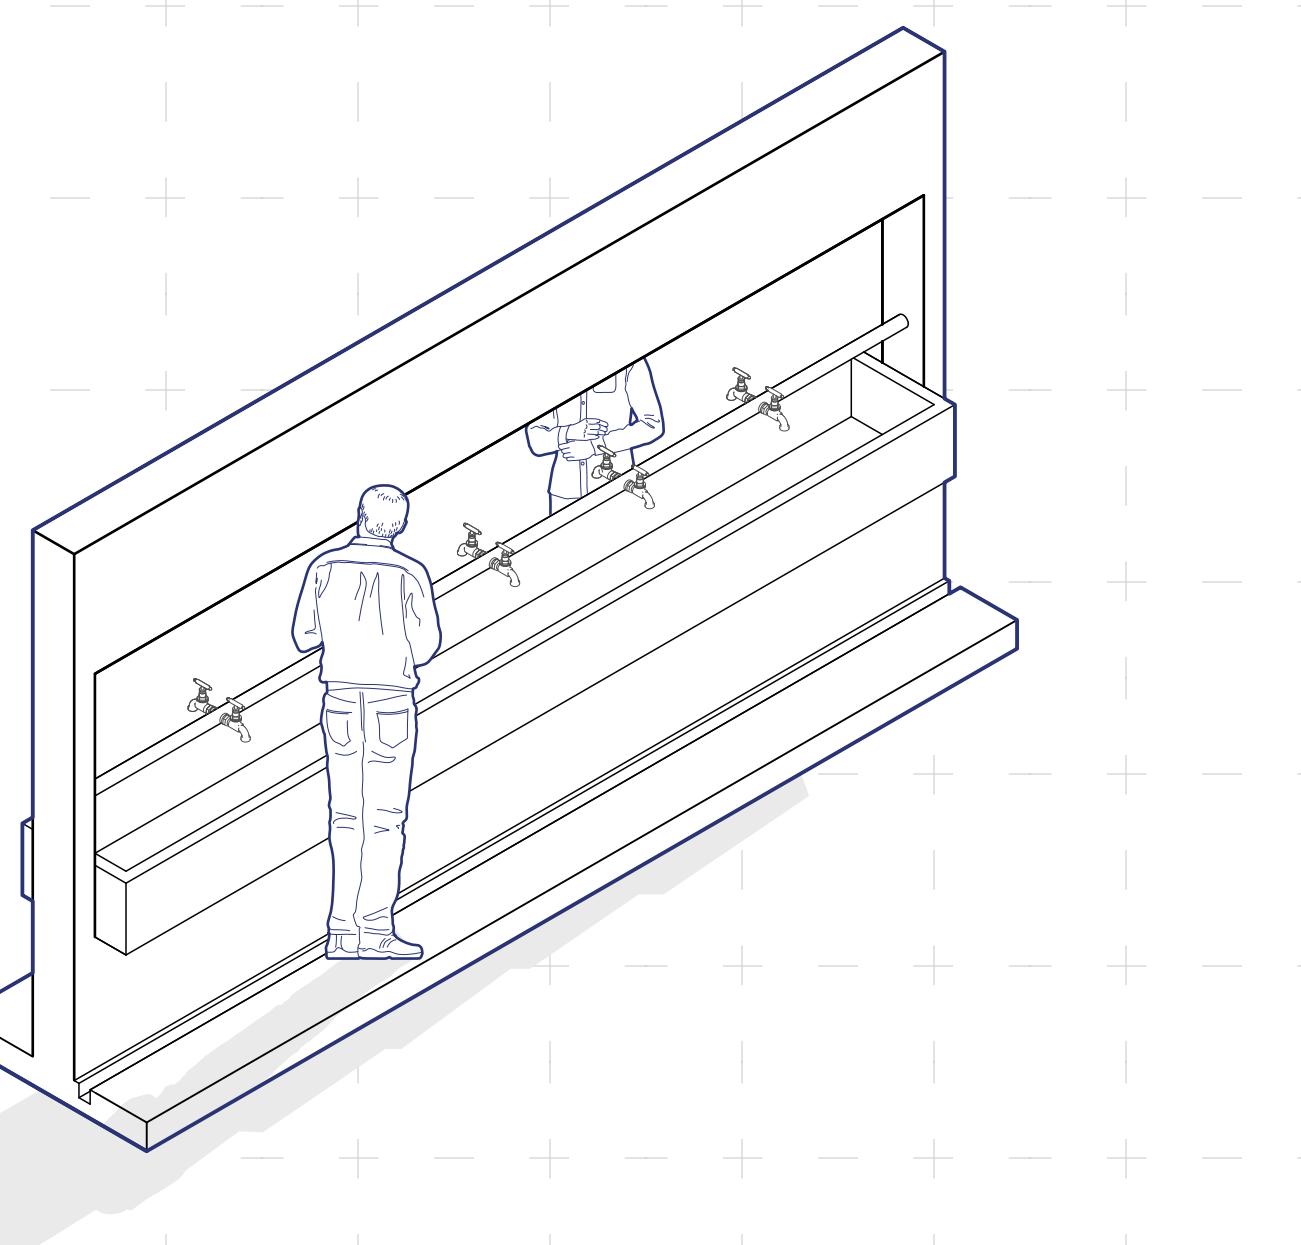


ショット

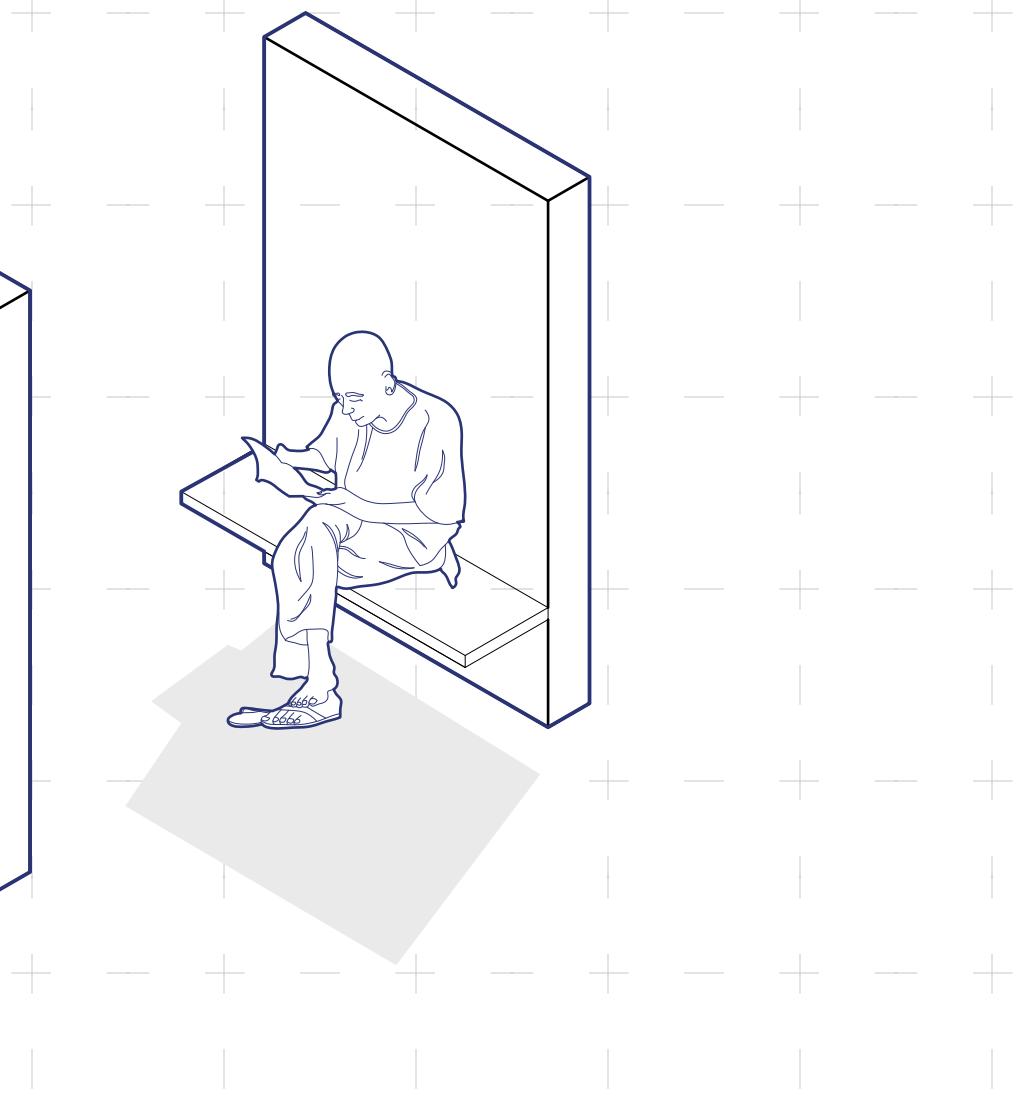


نشת אחסון  
ドボン

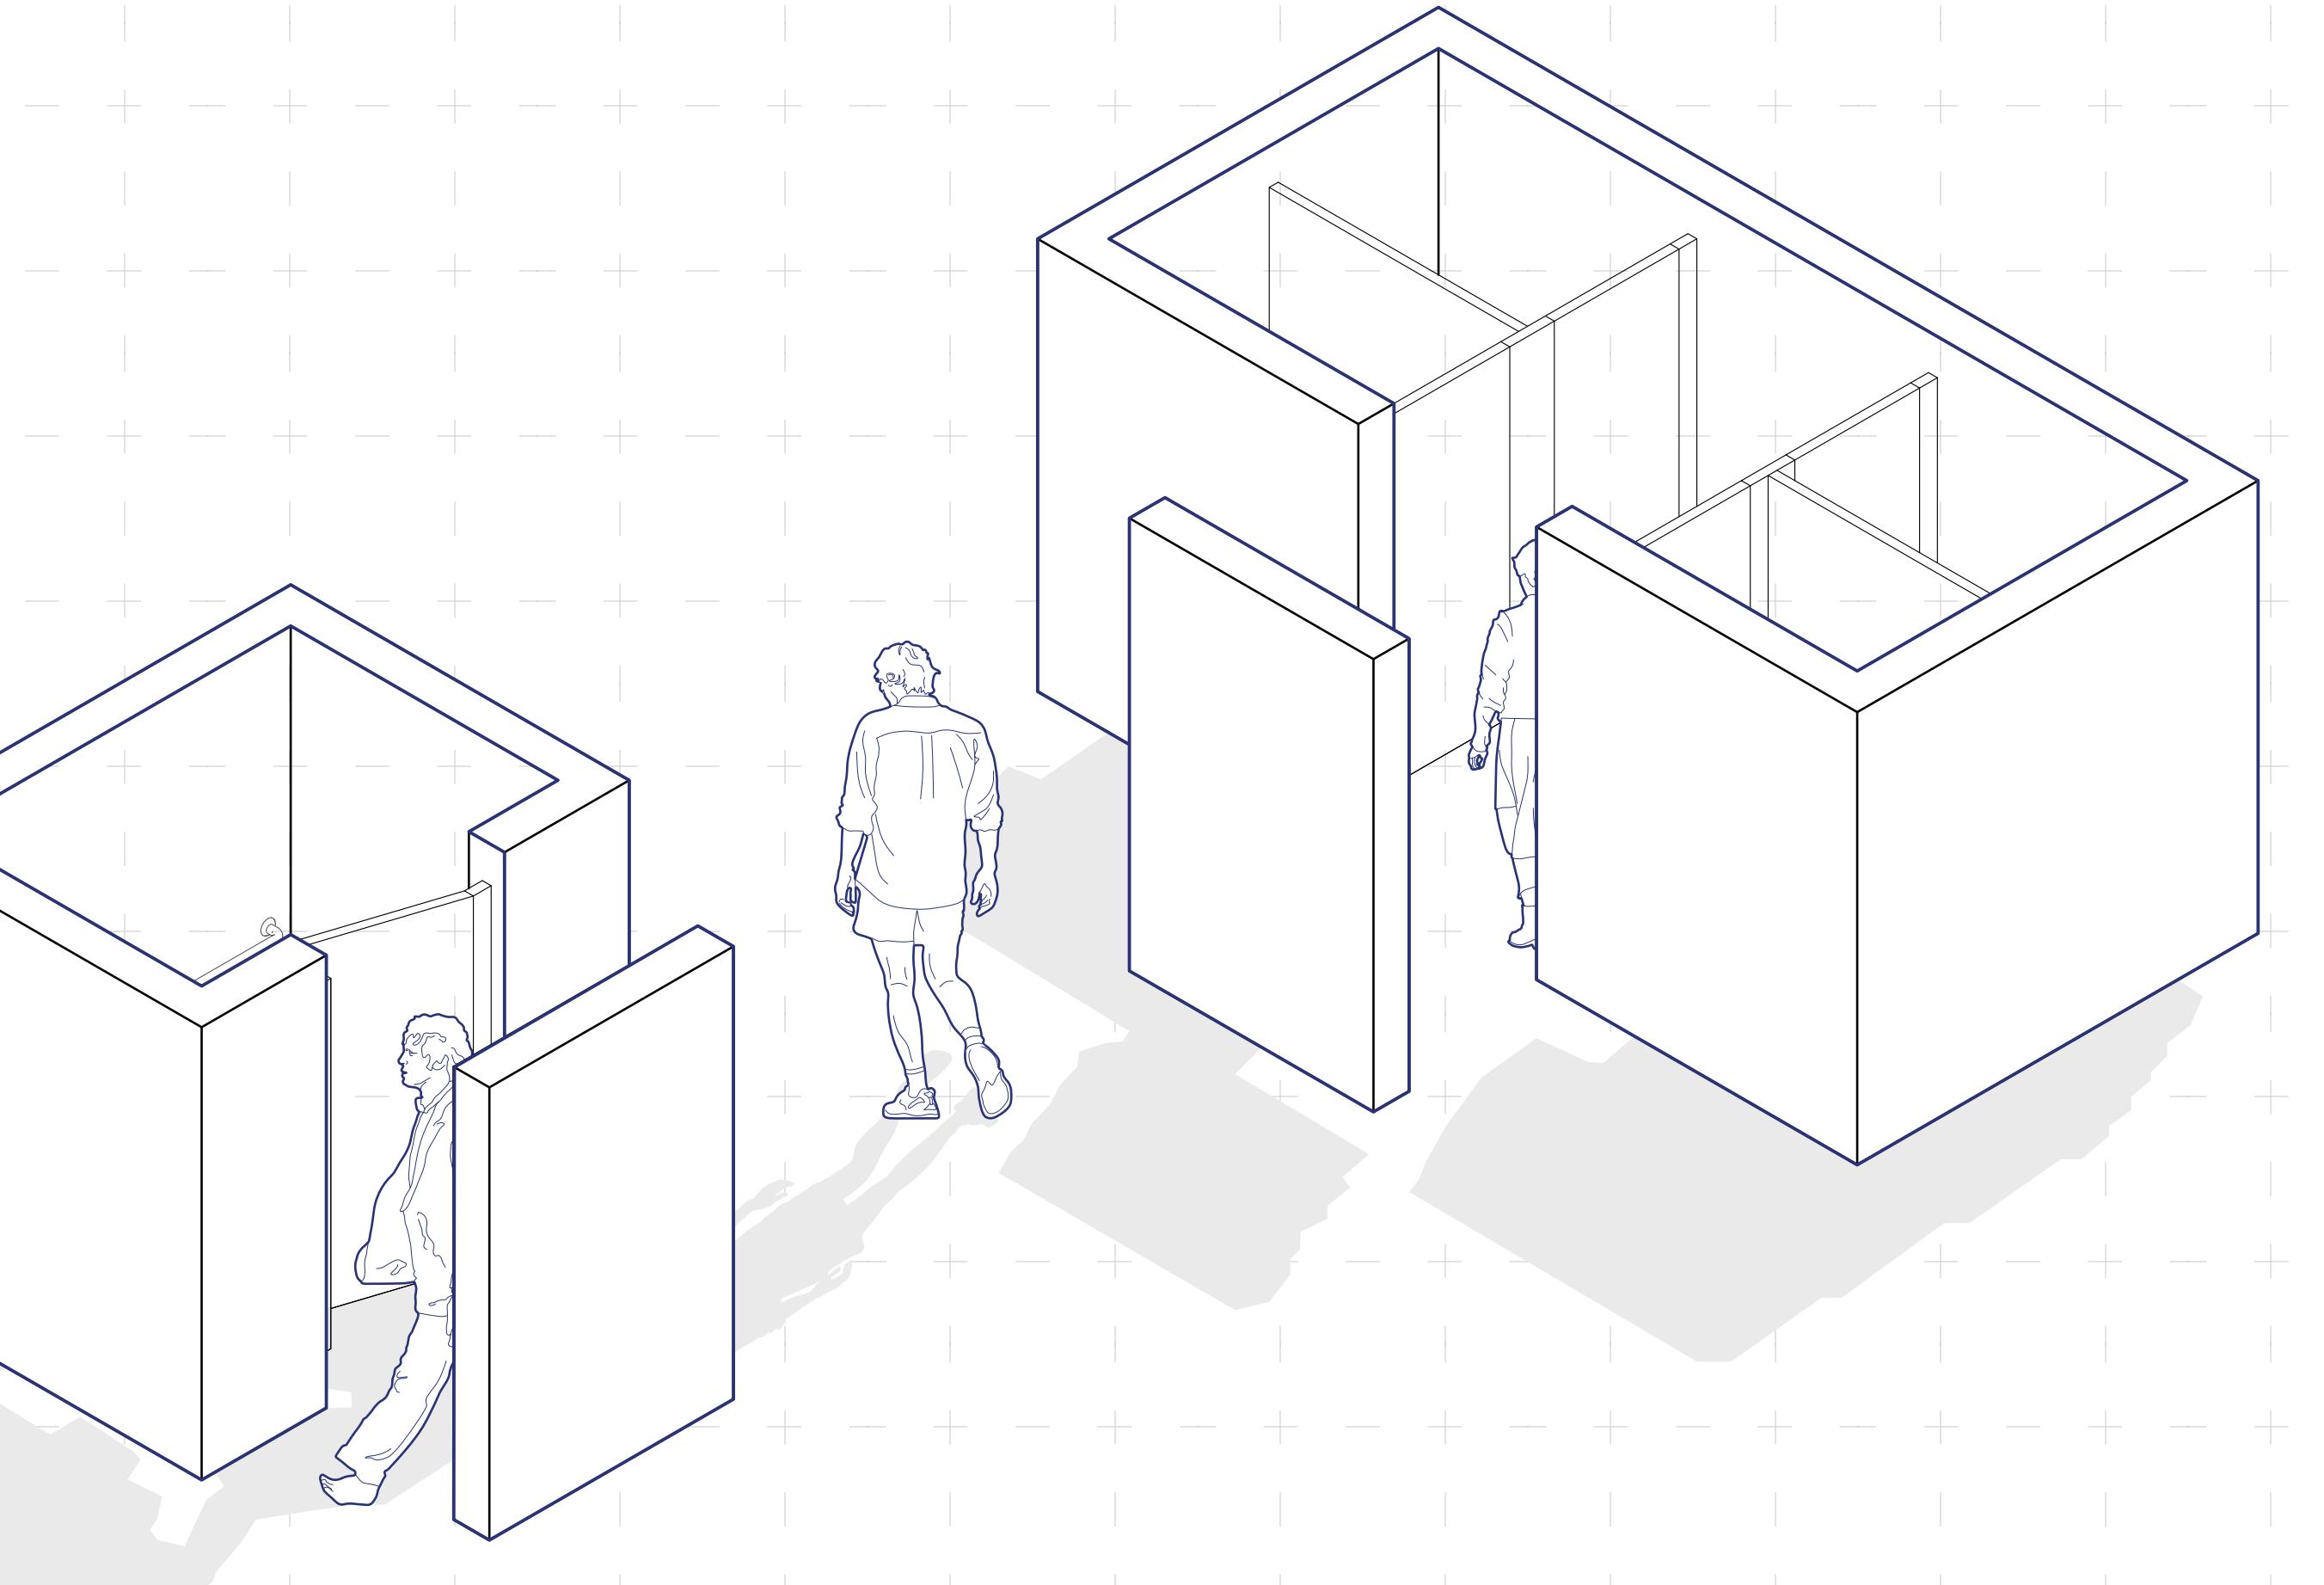


מערך קירות אלמנט הסתרה

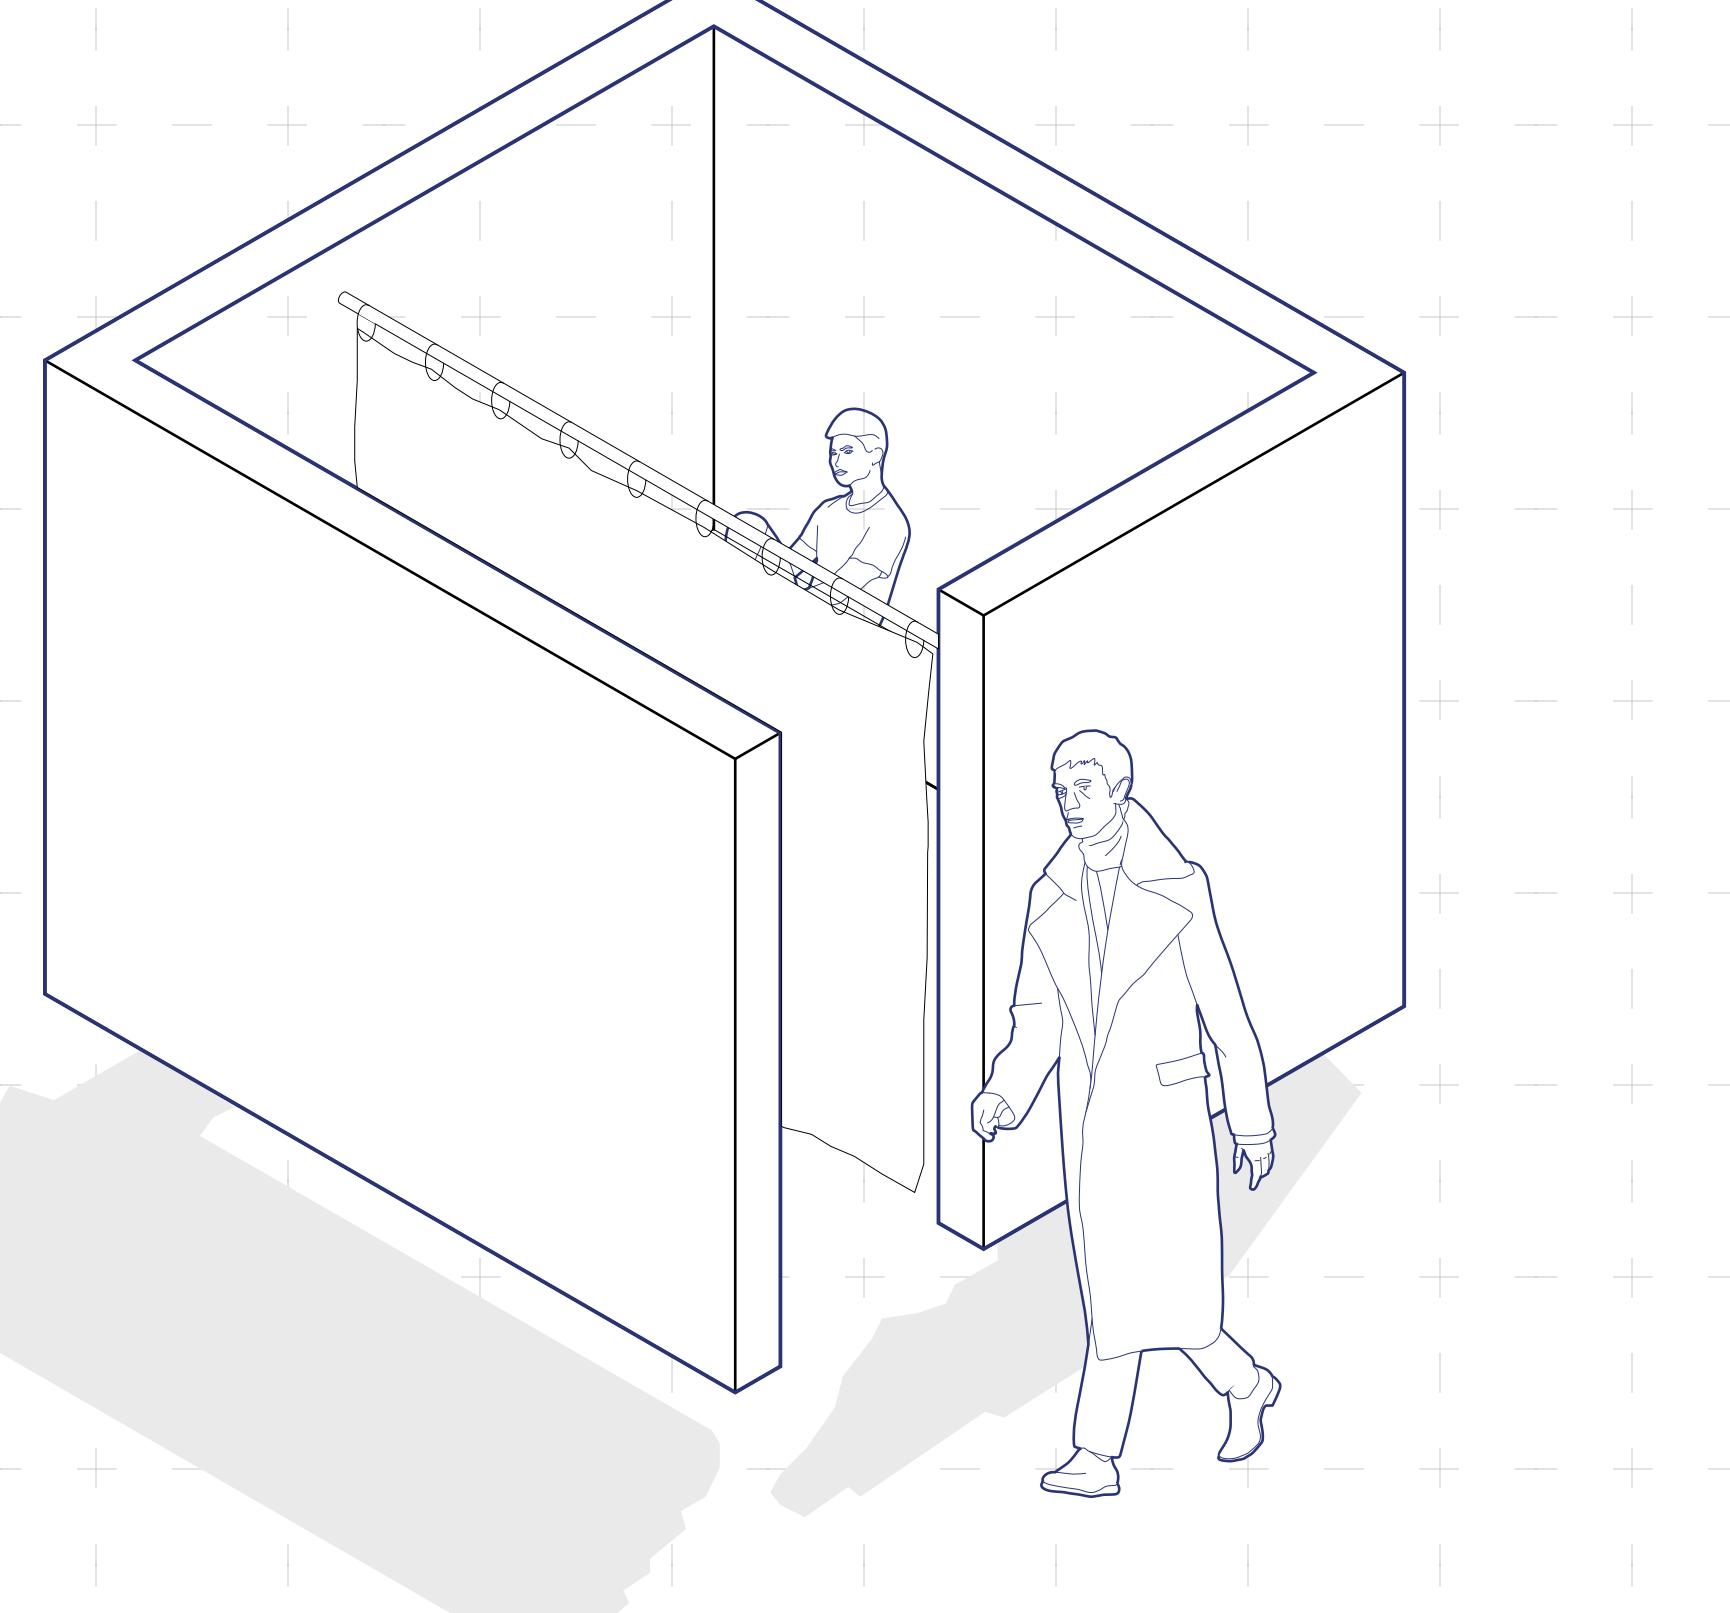

יחידה אנטימית לשימוש חירום

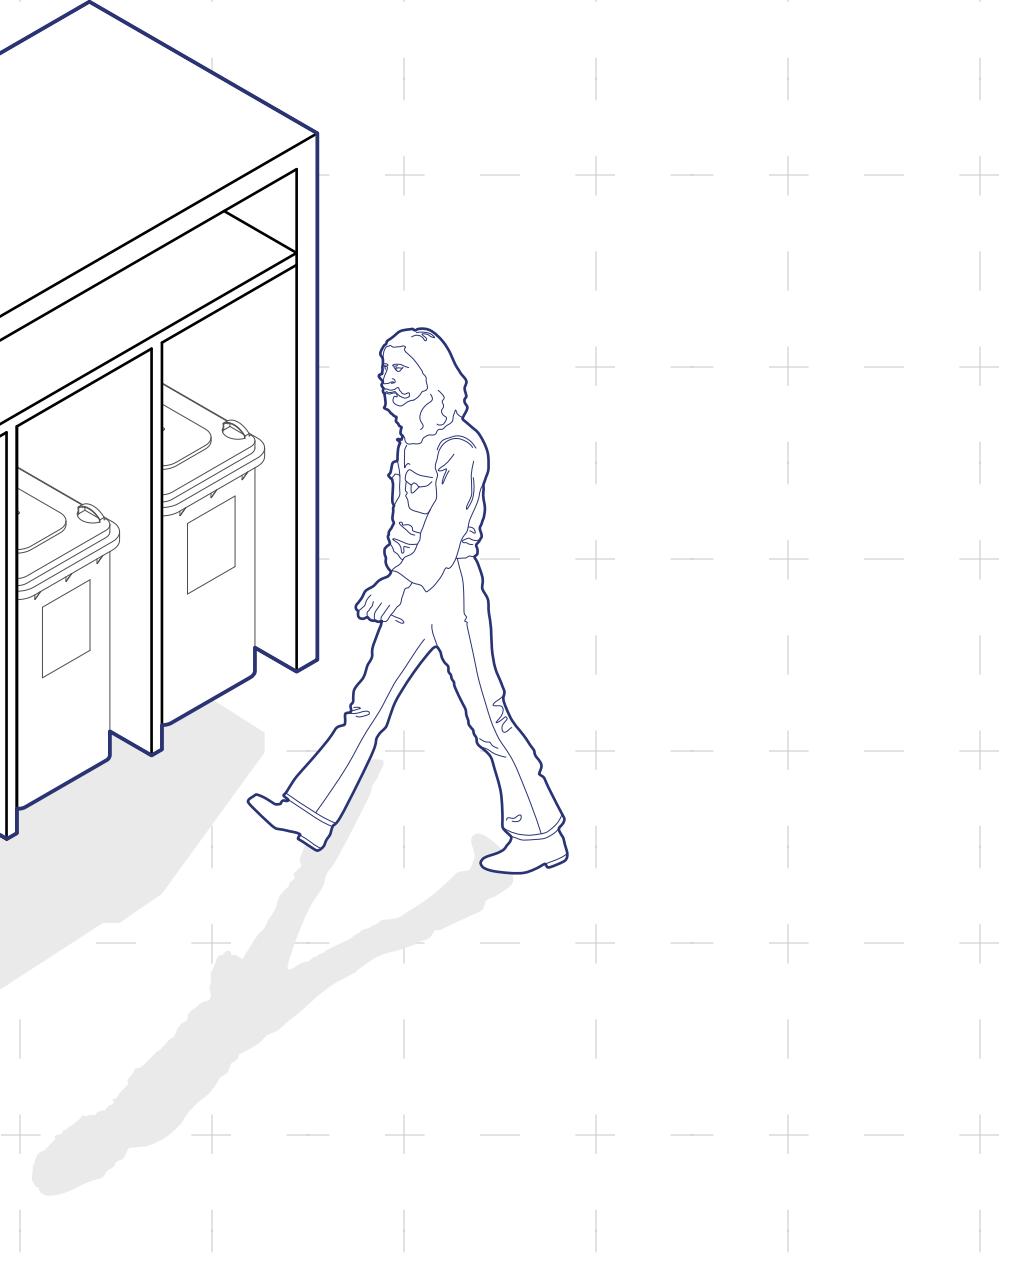


נישת אספה ומייחזר

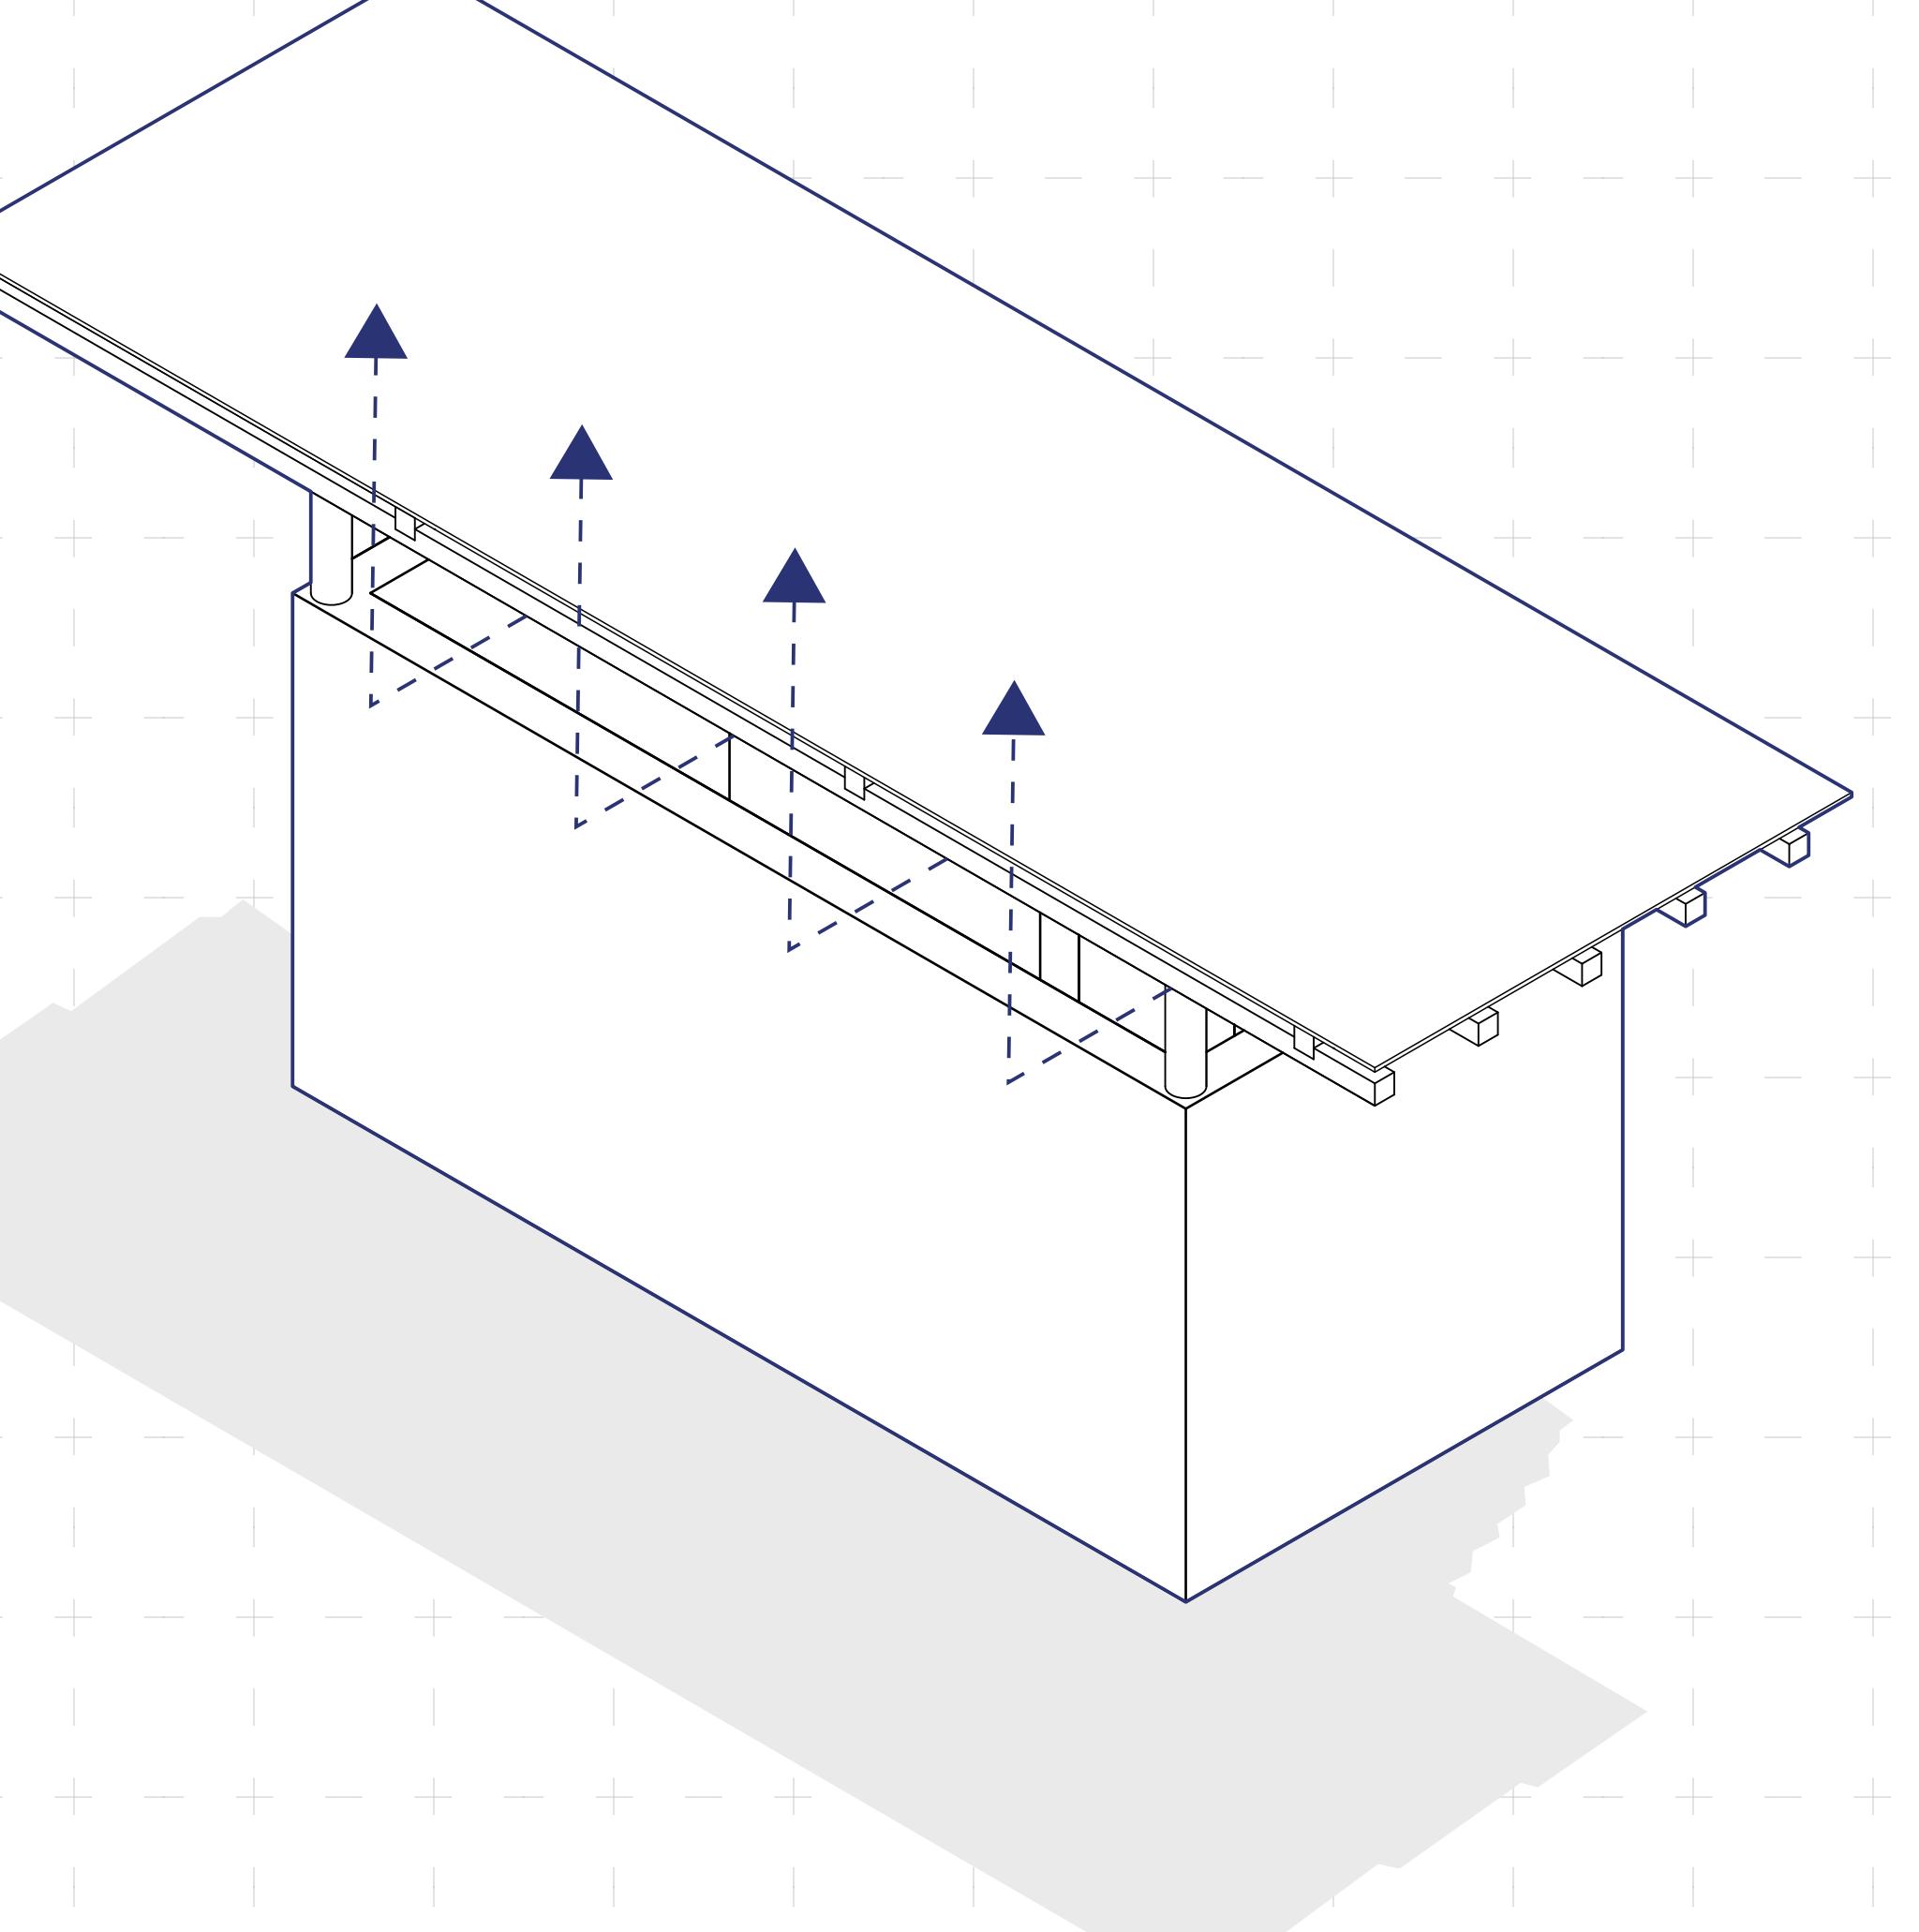


קורי מרחף

## סיעור רפואי | תכנית

 

## סיעור רפואי | תכנית

 

**סיעור רפואי | חתך**

